


Pohled jihozápadní - stávající stav

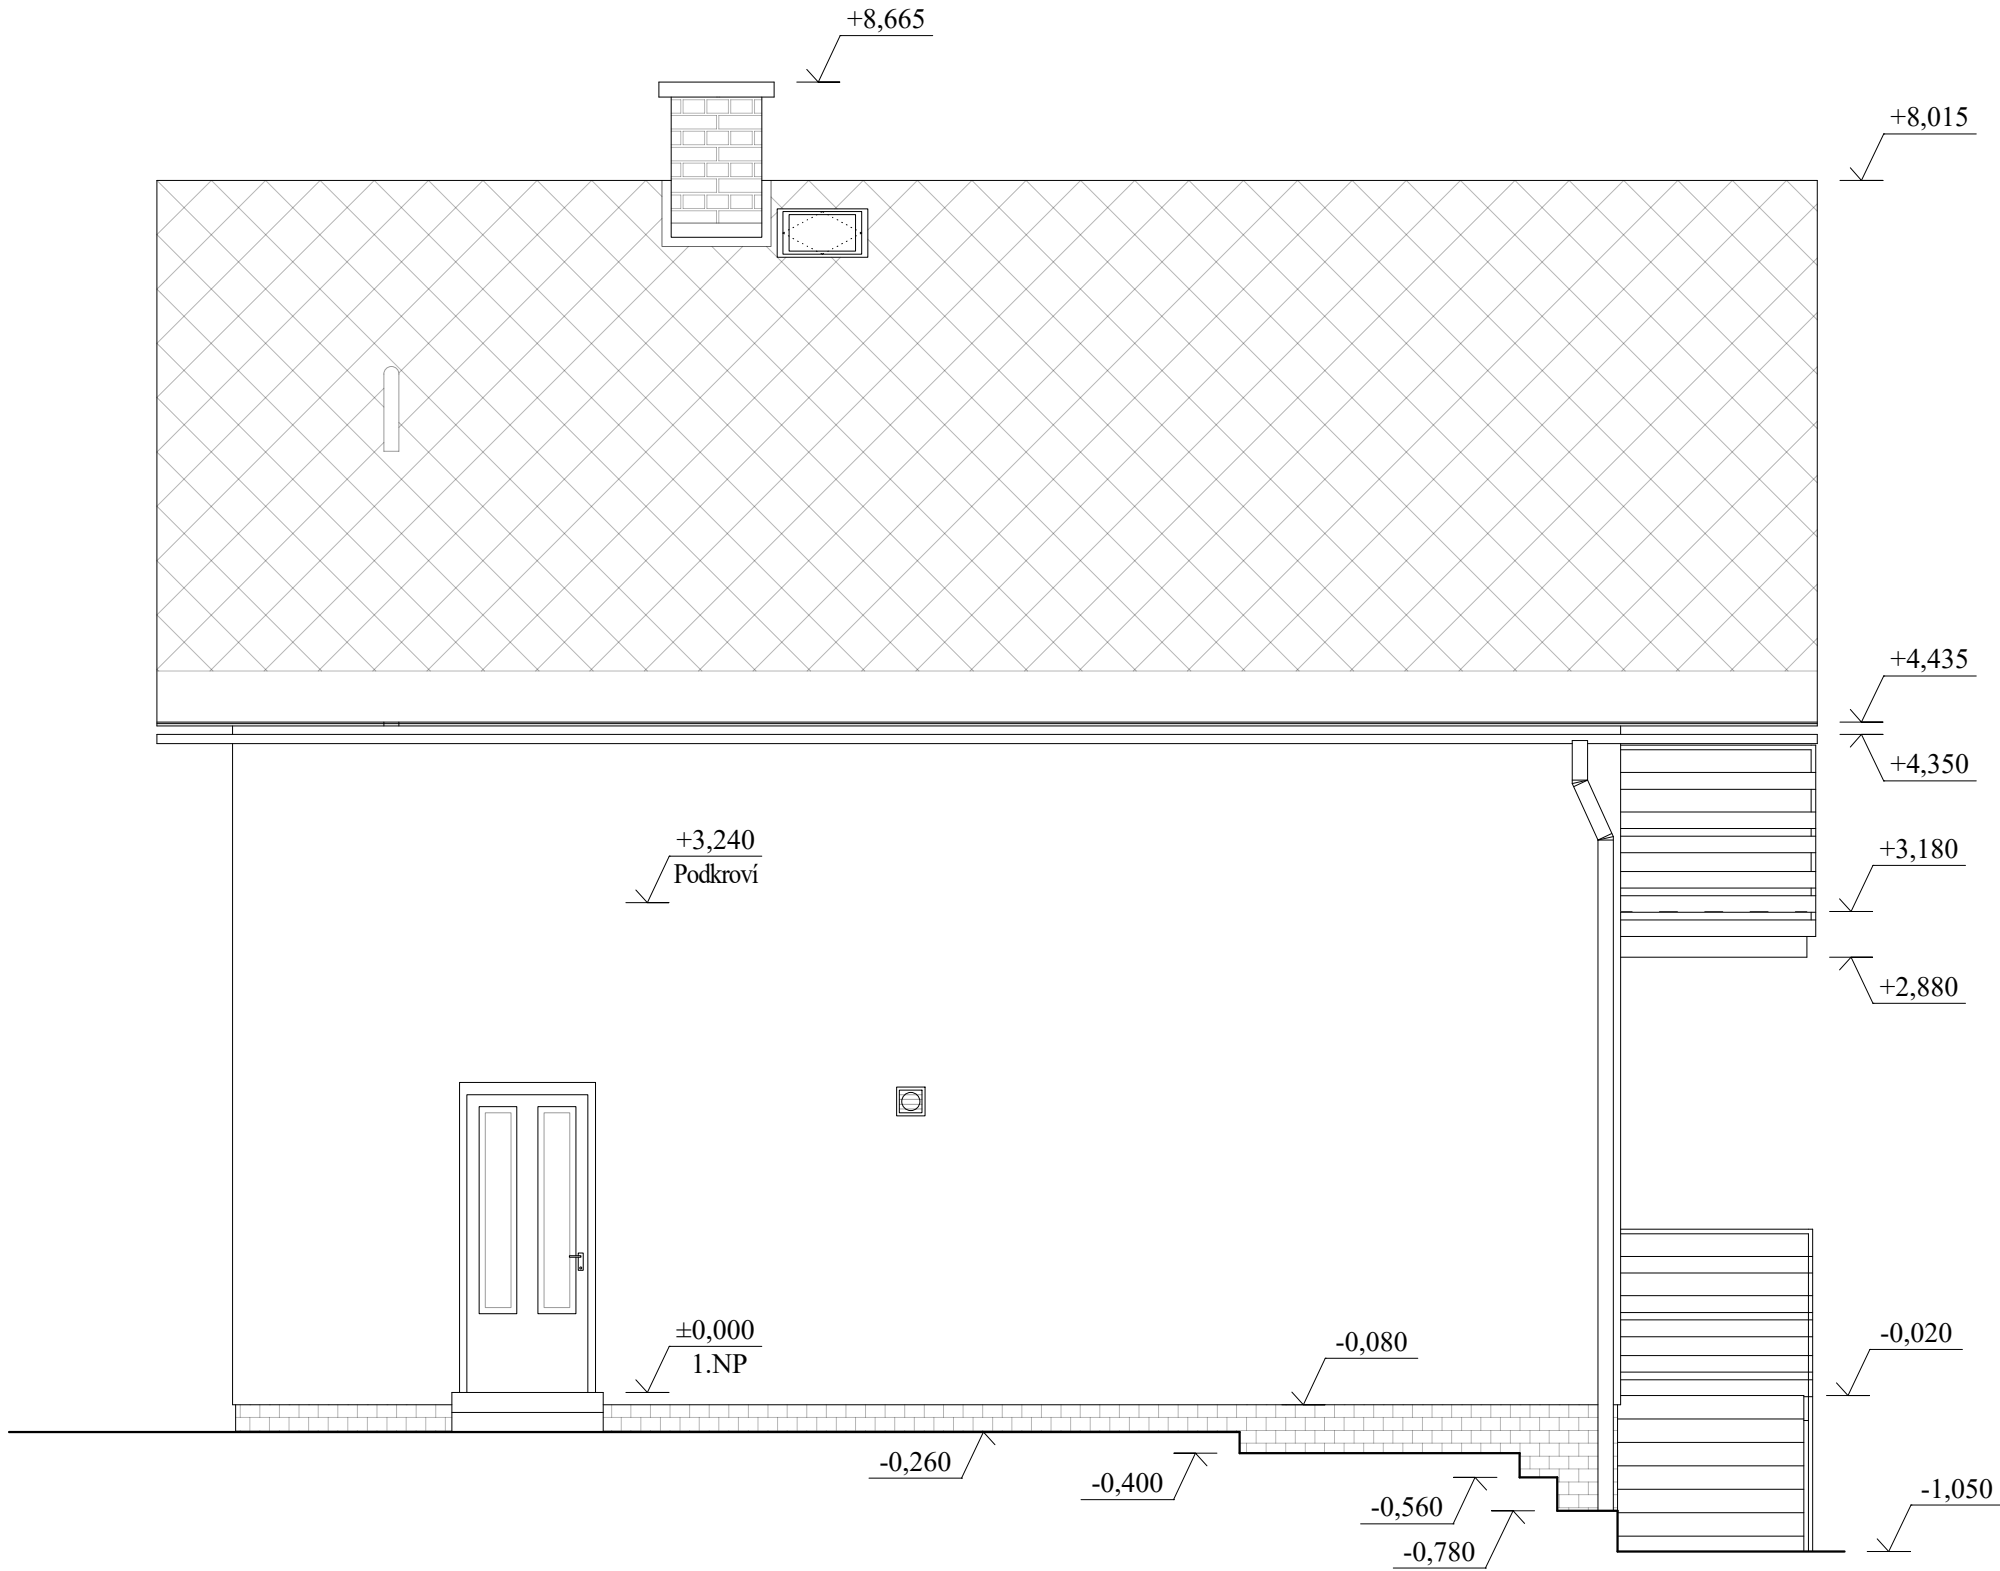

BAREVNÉ ŘEŠENÍ:	
FASÁDA - V PLOŠE	ODSTÍN ŠEDÉ
FASÁDA - SOKL	ODSTÍN ŽLUTÉ - KERA. OBKLAD
VÝPLNĚ OTVORŮ	ODSTÍN HNĚDÉ
TESAŘSKÉ PRVKY	ODSTÍN HNĚDÉ
STŘEŠNÍ KRYTINA	ODSTÍN TMAVĚ ČERVENÉ AŽ HNĚDÉ
KLEMPÍŘSKÉ PRVKY	ODSTÍN TMAVĚ ČERVENÉ AŽ HNĚDÉ

1.NP = ±0.000 = STÁVAJÍCÍ			
Vedoucí projektant:		Zodp. projektant:	
Ing. Radomír Hladký		Ing. Radomír Hladký	
Stavebník:		Ing. Lenka Kubínková, Donská 1261, Liberec XXX-Vratislavice nad Nisou, 46311 Liberec	
Místo stavby:		p.p.č. 2174, k.ú. Vratislavice nad Nisou [785644]	
Akce:		Pasport rodinného domu - Donská č.p. 868, Liberec XXX - Vratislavice nad Nisou	
Objekt:		Stavební část	
Výkres:		Pohled jihozápadní - stávající stav	
Formát:		594 x 297	
Datum:		04/2026	
Stupeň:		Pasport	
Měřítko:		Číslo výkresu:	
1:50		D.1-08	