


Pohled severozápadní - stávající stav

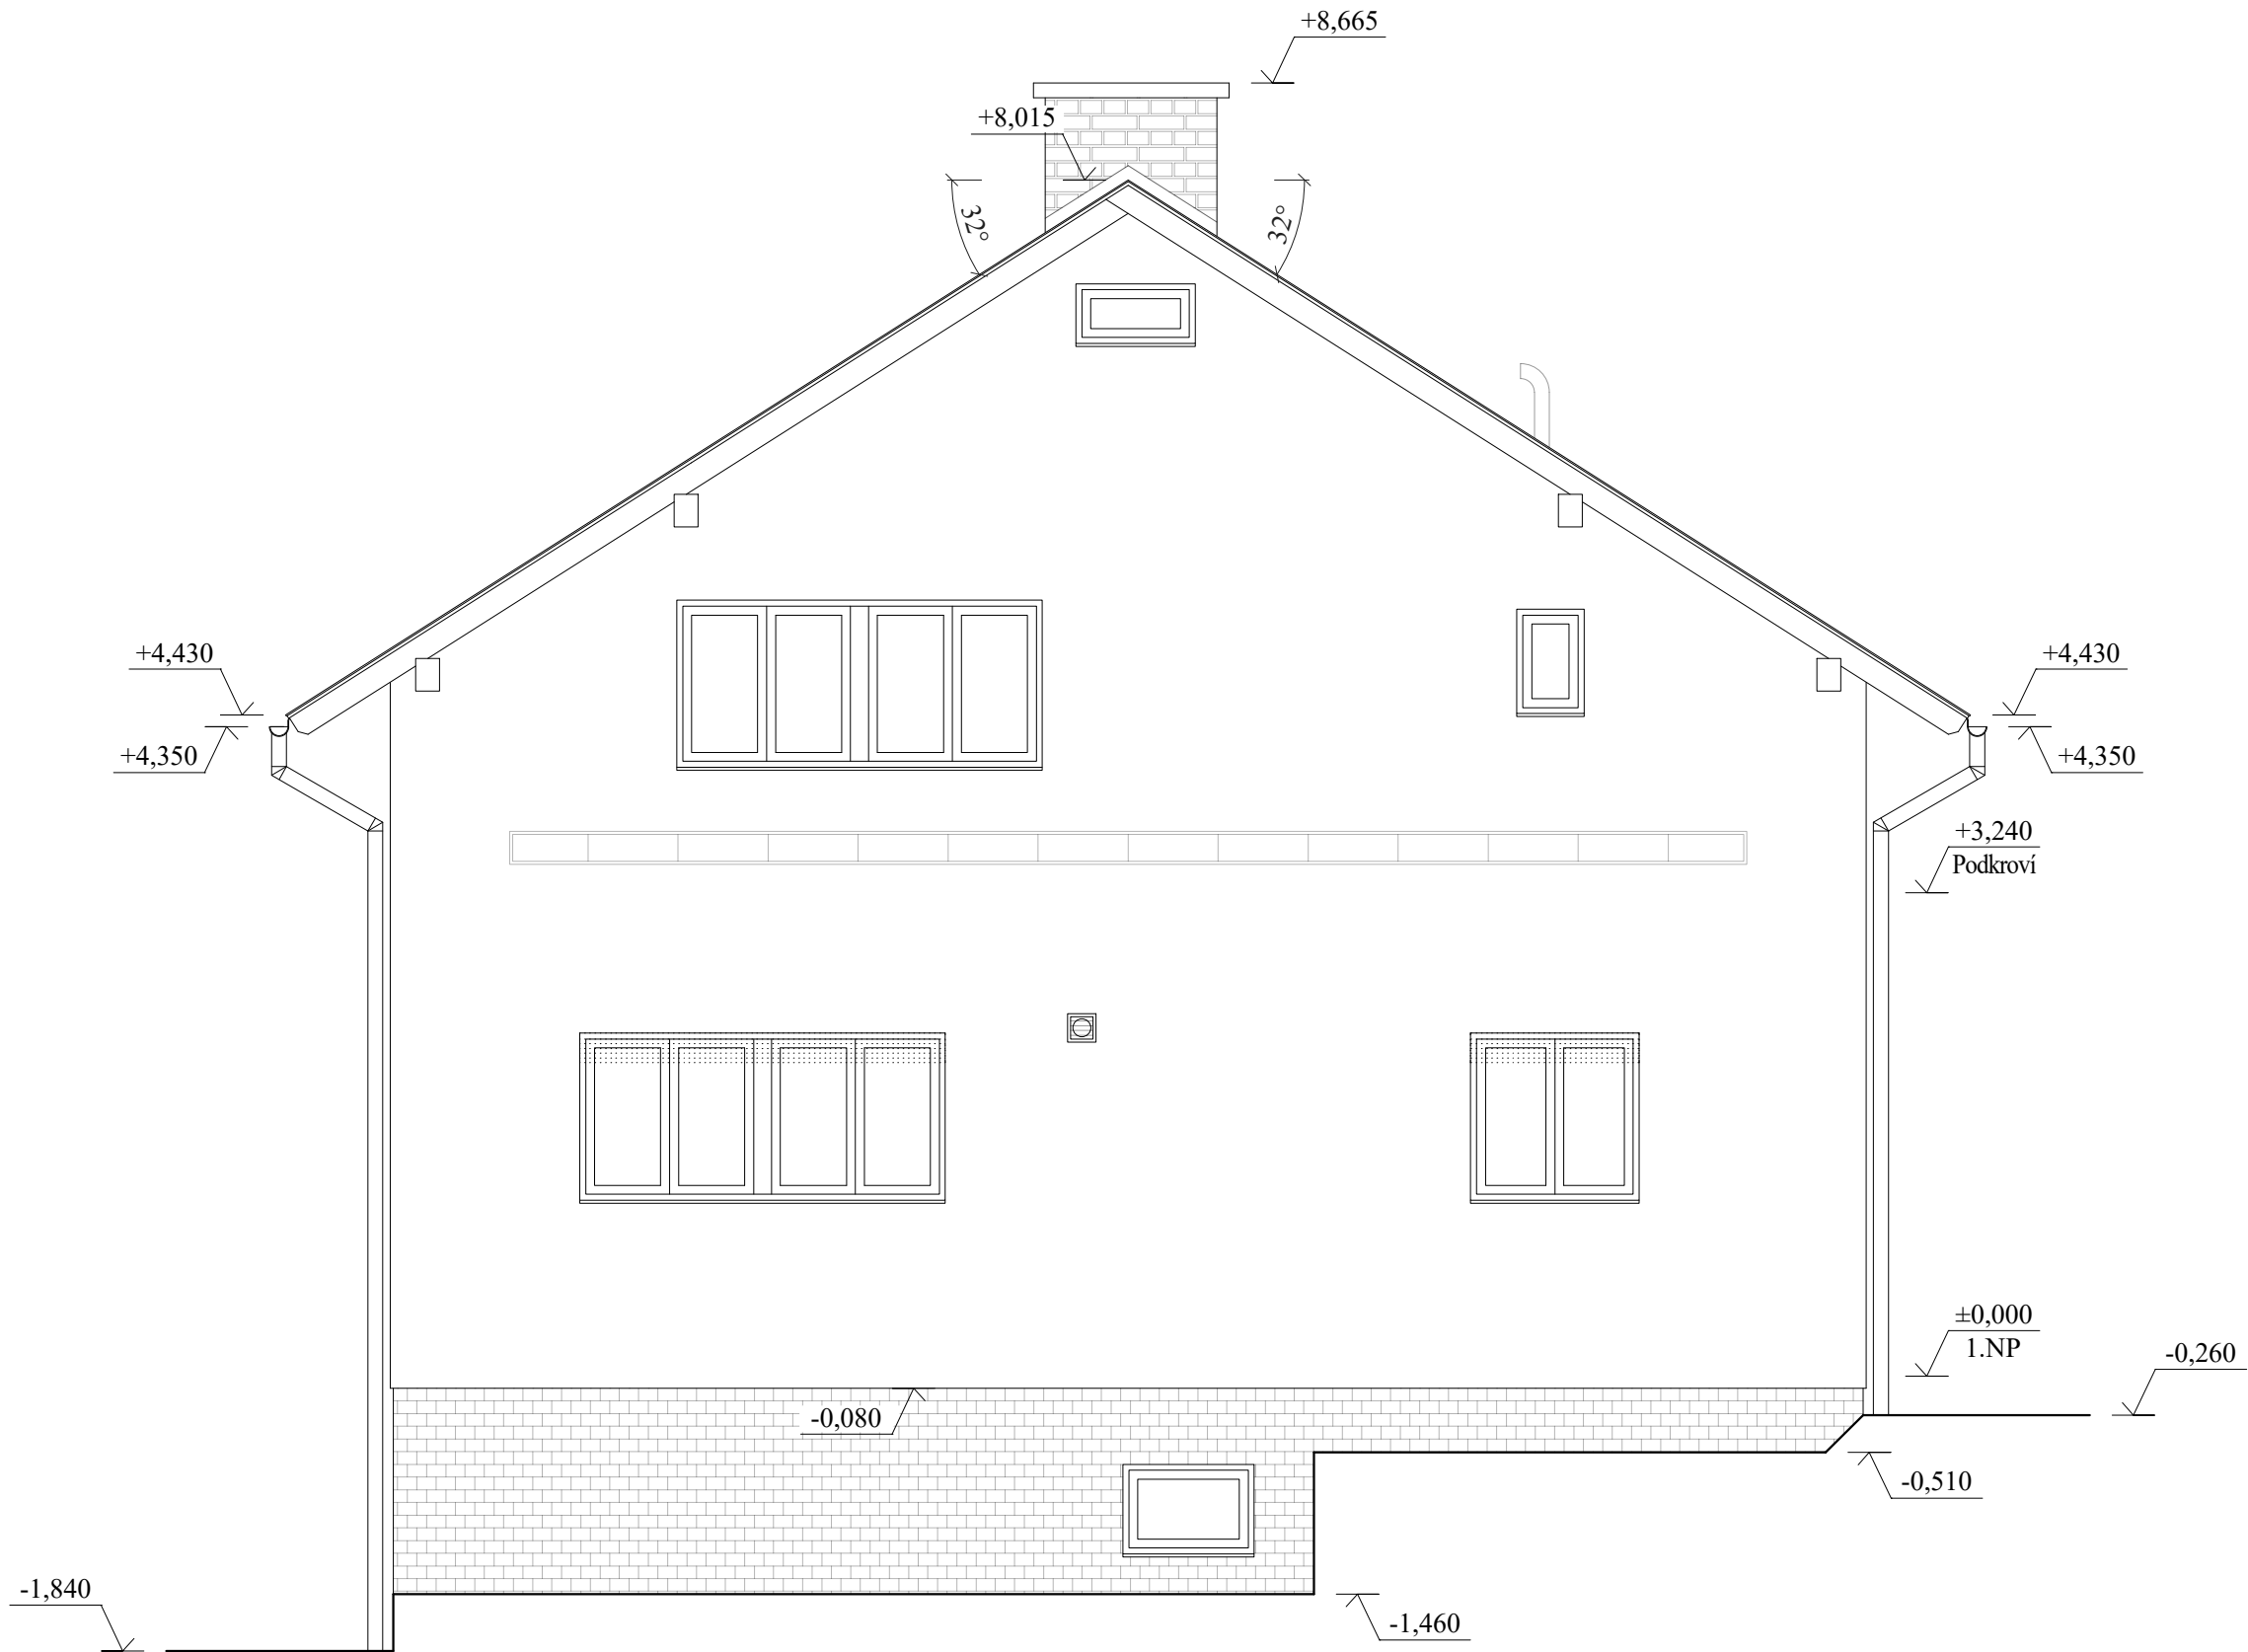

- BAREVNÉ ŘEŠENÍ:

FASÁDA - V PLOŠE

FASÁDA - SOKL

VÝPLNĚ OTVORŮ

TESAŘSKÉ PRVKY

STŘEŠNÍ KRYTINA

KLEMPÍŘSKÉ PRVKY
- ODSTÍN ŠEDÉ

ODSTÍN ŽLUTÉ - KERA. OBKLAD

ODSTÍN HNĚDÉ

ODSTÍN HNĚDÉ

ODSTÍN TMAVĚ ČERVENÉ AŽ HNĚDÉ

ODSTÍN TMAVĚ ČERVENÉ AŽ HNĚDÉ



Podepsal Ing. Radomír Hladký

1.NP = ±0.000
= STÁVAJÍCÍ

Vedoucí projektant:	Zodp. projektant:	Vypracoval:	Ing. Radim Hladký projektová činnost ve výstavbě	
Ing. Radomír Hladký	Ing. Radomír Hladký	Ing. Radim Hladký		
Stavebník:	Ing. Lenka Kubínková, Donská 1261, Liberec XXX-Vratislavice nad Nisou, 46311 Liberec			Český Dub, Na Žižkově 154 / IV ☎ +420 734 483 208 ✉ radim-hladky@seznam.cz
Místo stavby:	p.p.č. 2174, k.ú. Vratislavice nad Nisou [785644]			
Akce:	Pasport rodinného domu - Donská č.p. 868, Liberec XXX - Vratislavice nad Nisou			Formát: 594 x 297
Objekt:	Stavební část			Datum: 04/2026
Výkres:	Pohled severozápadní - stávající stav			Stupeň: Pasport
				Měřítko: 1:50
				Číslo výkresu: D.1-09