



Půdorys 1.PP - stávající stav

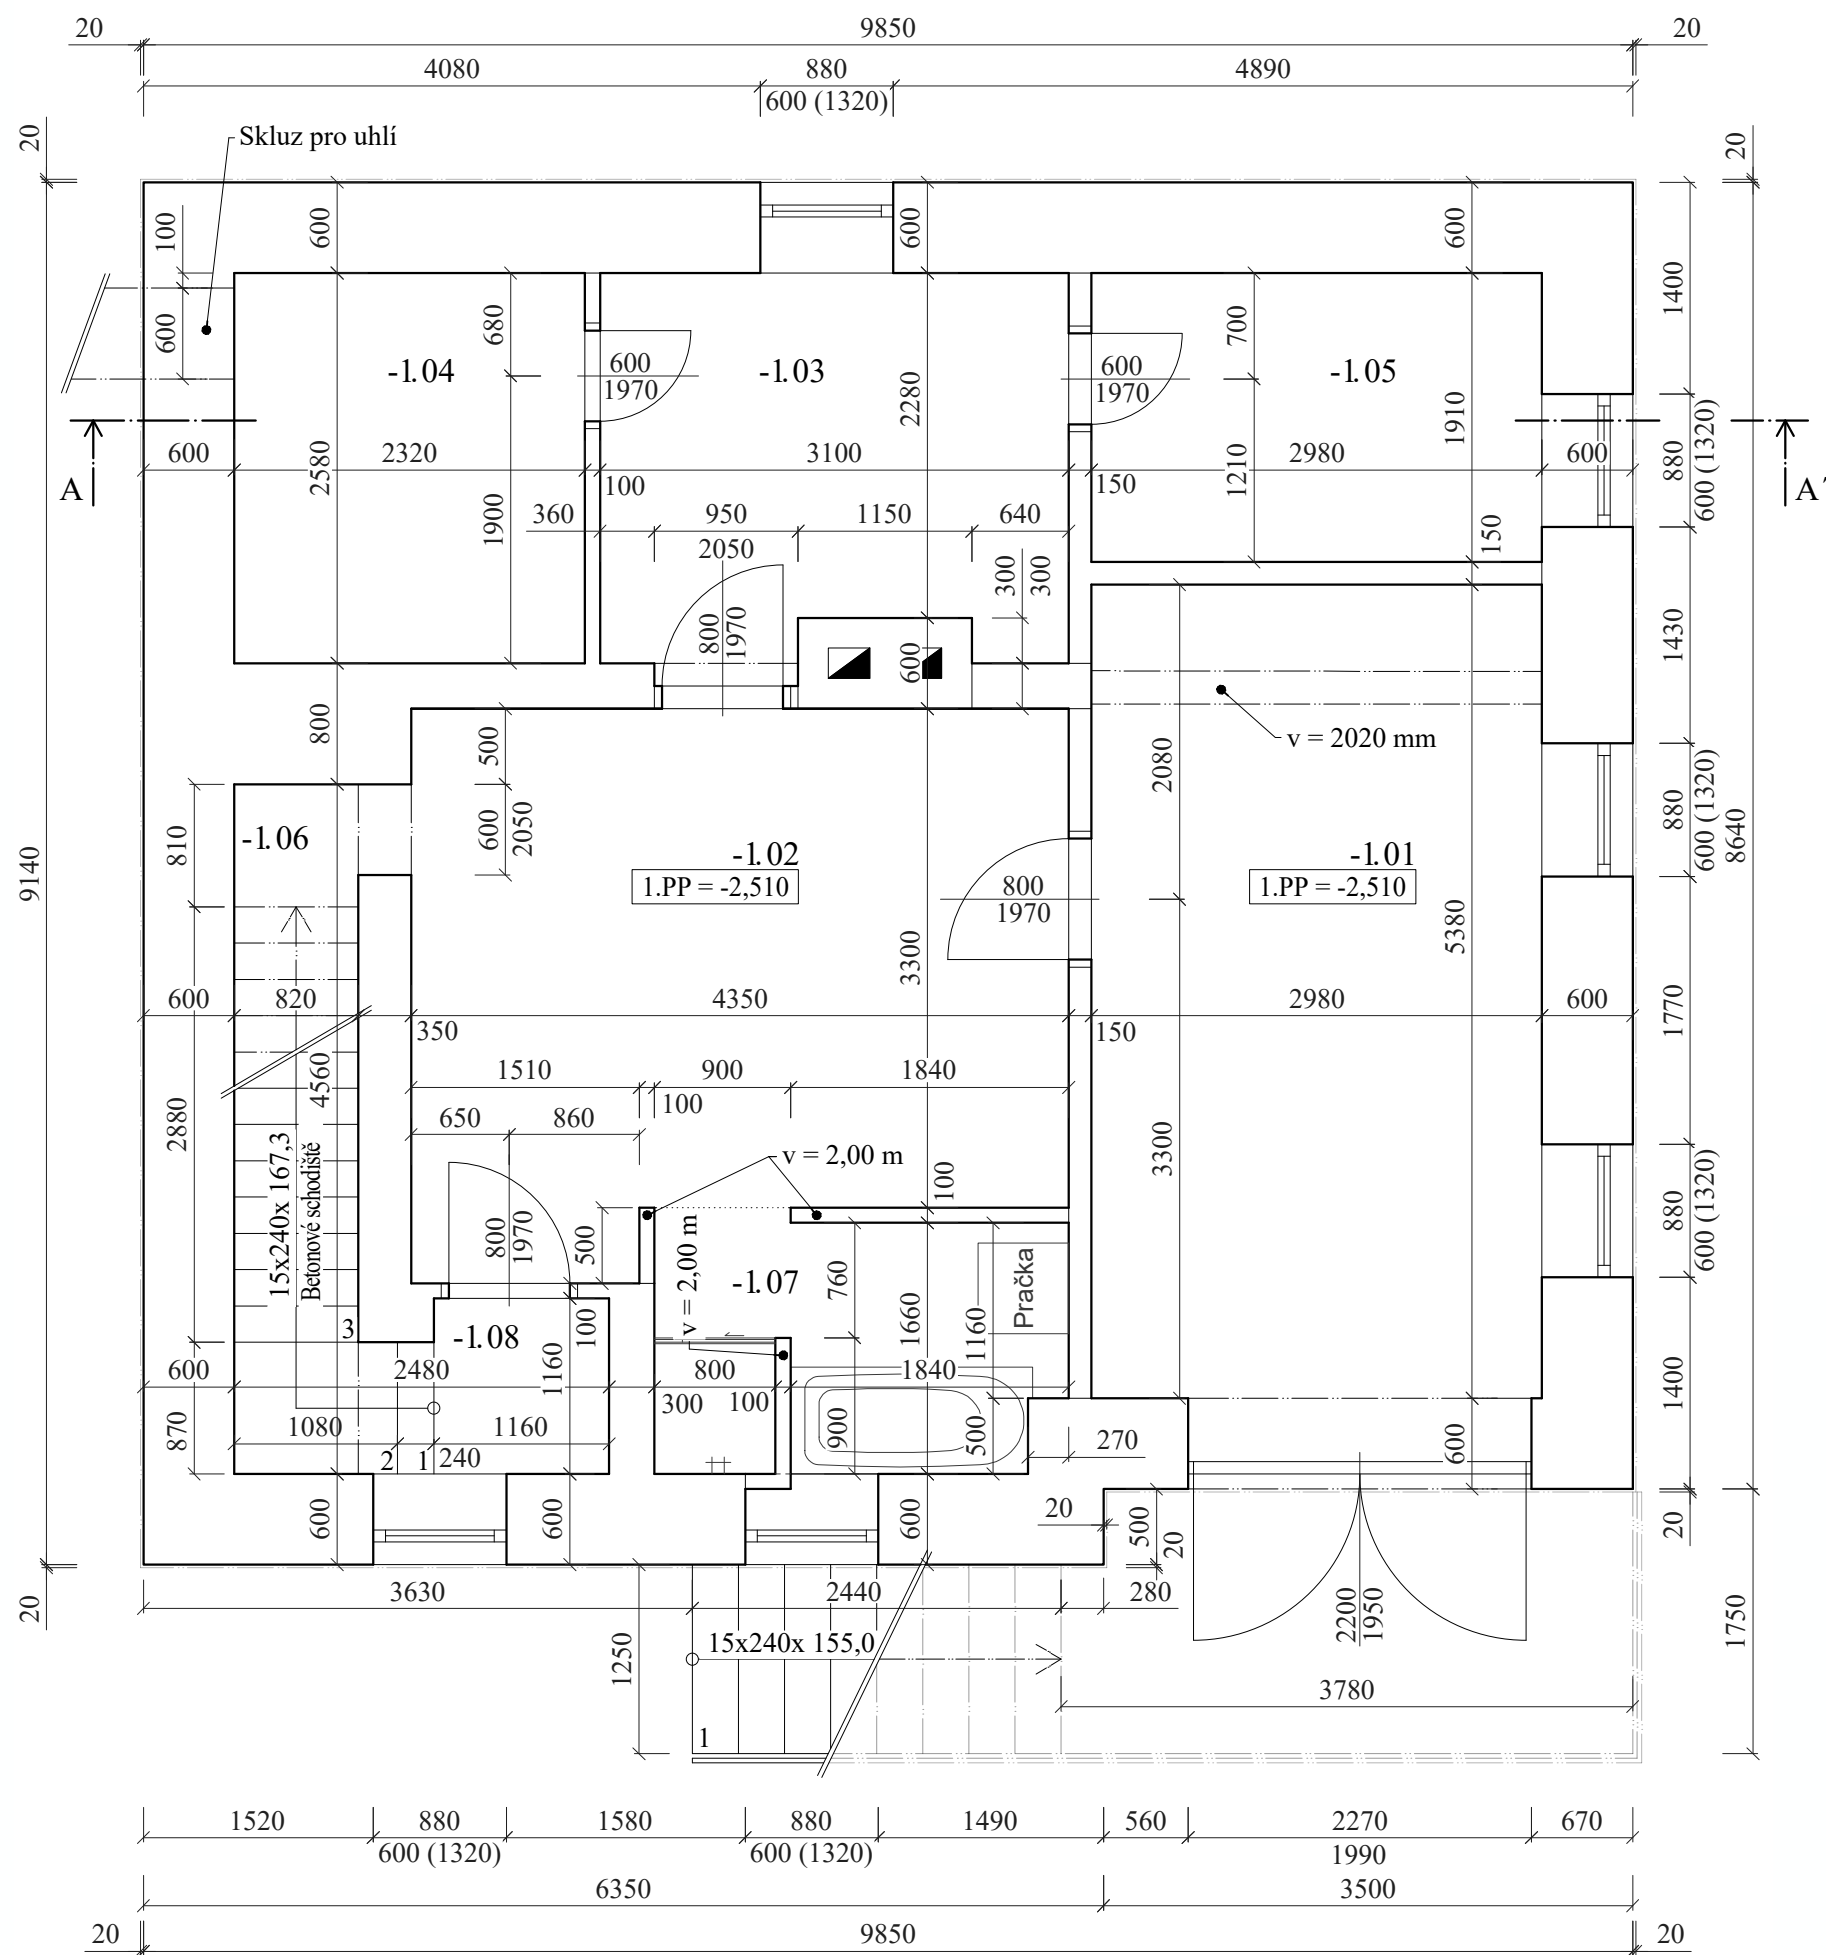

TABULKA MÍSTNOSTÍ					
Číslo místn.	Název místnosti	Plocha [m²]	Výška místnosti	Podlaha	Poznámka
-1.01	Garáž	16,03	2220 mm	Betonová mazanina	
-1.02	Chodba	15,11	2270 mm	Keramiocká dlažba	
-1.03	Kotelna	7,65	2270 mm	Betonová mazanina	
-1.04	Uhelna	5,99	2270 mm	Betonová mazanina	
-1.05	Sklep	5,69	2270 mm	Betonová mazanina	
-1.06	Komora	1,84	2270 mm	Betonová mazanina	S.v. míst. omezena - pod schodištěm
-1.07	Umývárna	4,41	2270 mm	Keramiocká dlažba	Kera. obklad, v=1400 mm
-1.08	Chodba + schodiště	6,27	2270 mm	Betonová mazanina	


LEGENDA KONSTRUKCÍ:

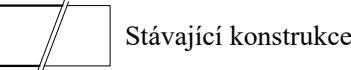

Stávající konstrukce



Podepsal Ing. Radomír Hladký

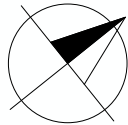

1.NP = ±0.000
= STÁVAJÍCÍ

Vedoucí projektant:	Zodp. projektant:	Vypracoval:	Ing. Radim Hladký projektová činnost ve výstavbě	
Ing. Radomír Hladký	Ing. Radomír Hladký	Ing. Radim Hladký		
Stavebník:	Ing. Lenka Kubínková, Donská 1261, Liberec XXX-Vratislavice nad Nisou, 46311 Liberec		Český Dub, Na Žižkově 154 / IV +420 734 483 208 radim-hladky@seznam.cz	
Místo stavby:	p.p.č. 2174, k.ú. Vratislavice nad Nisou [785644]		Formát:	420 x 297
Akce:	Pasport rodinného domu - Donská č.p. 868, Liberec XXX - Vratislavice nad Nisou		Datum:	04/2026
Objekt:	Stavební část		Stupeň:	Pasport
Výkres:	Půdorys 1.PP - stávající stav		Měřítko:	Číslo výkresu: 1:50 D.1-01