



Půdorys 1.NP - stávající stav

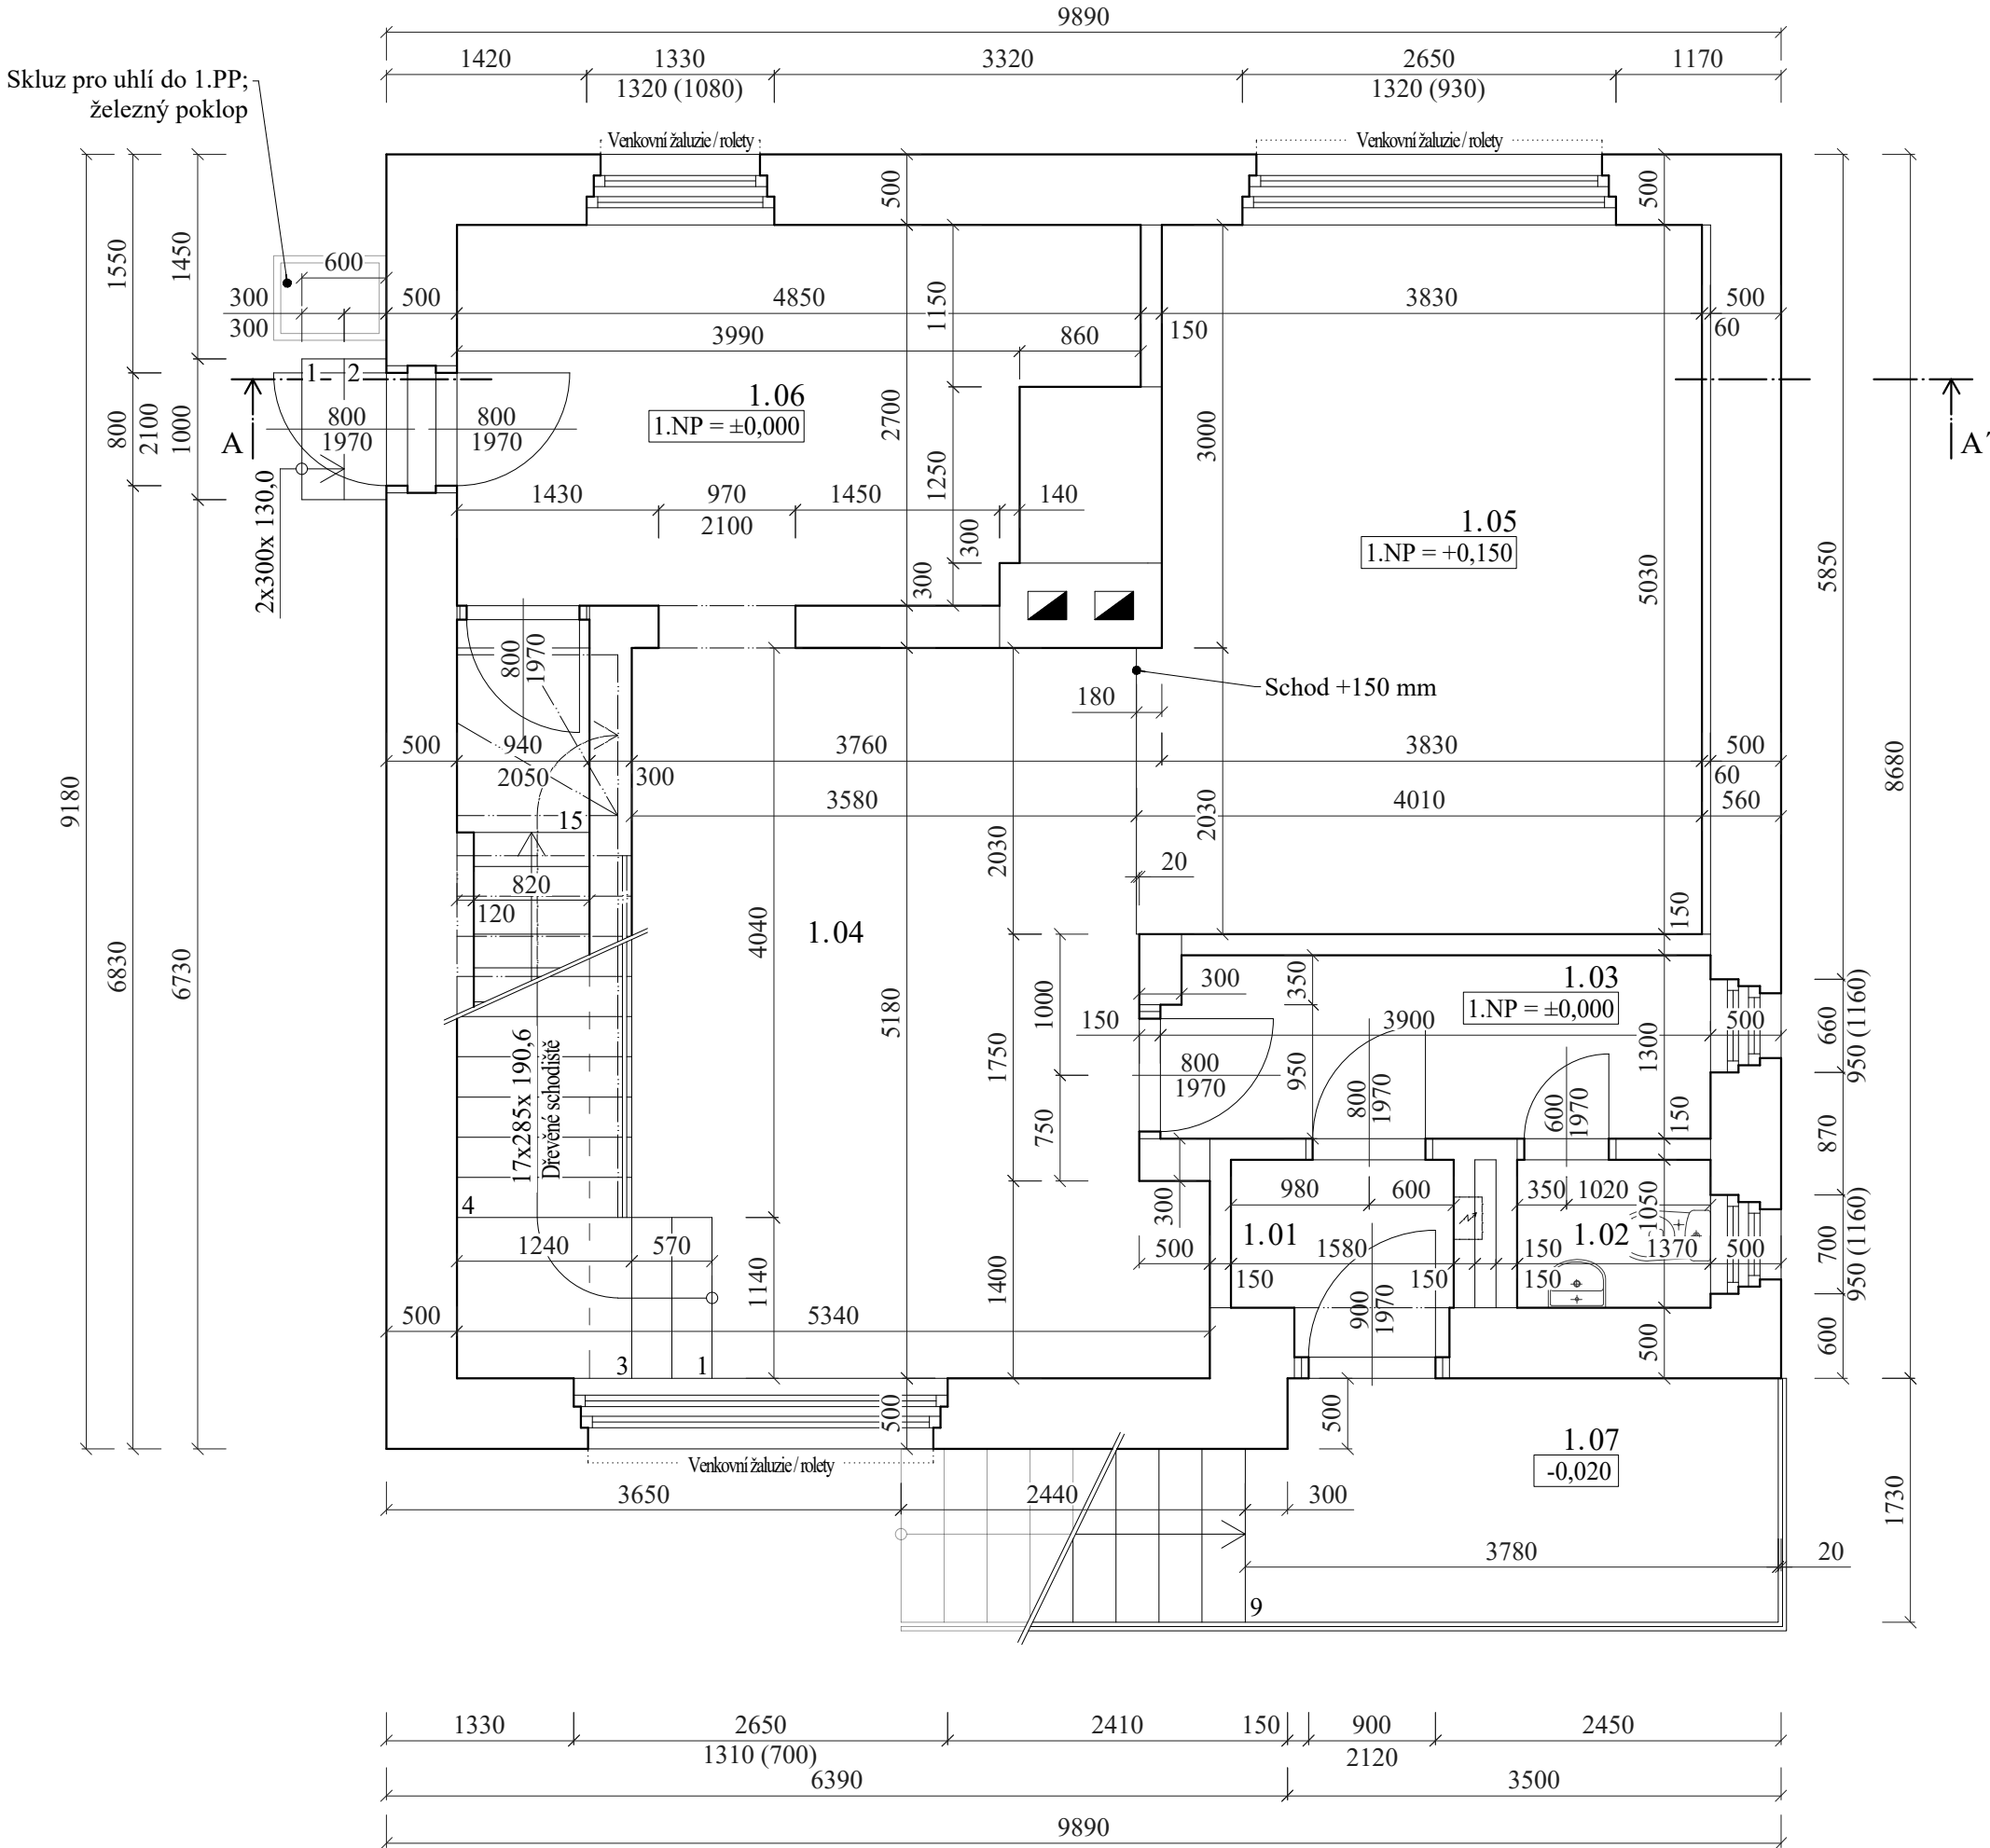

TABULKA MÍSTNOSTÍ

Číslo místn.	Název místnosti	Plocha [m²]	Výška místnosti	Podlaha	Poznámka
1.01	Zádvěří	1,66	2720 mm	Keramická dlažba	
1.02	WC	1,44	2720 mm	Keramická dlažba	Kera. obklad, v=1400 mm
1.03	Chodba	5,02	2720 mm	Keramická dlažba	
1.04	Jídelna	25,27	2560 mm	Dřevěné vlysy	Trámový strop, v. bednění = 2700 mm
1.05	Obývací pokoj	19,63	2580 mm	Dřevěné vlysy	
1.06	Kuchyně	11,72	2750 mm	Keramická dlažba	Kera. obklad za původní kuch. linkou
1.07	Venkovní schodiště	9,39	2900 mm	Keramická dlažba	

LEGENDA KONSTRUKCÍ:

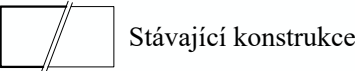

1.NP = ±0.000
= STÁVAJÍCÍ

Vedoucí projektant:	Zodp. projektant:	Vypracoval:
Ing. Radomír Hladký	Ing. Radomír Hladký	Ing. Radim Hladký
Stavebník:	Ing. Lenka Kubínková, Donská 1261, Liberec XXX-Vratislavice nad Nisou, 46311 Liberec	
Místo stavby:	p.p.č. 2174, k.ú. Vratislavice nad Nisou [785644]	
Akce:	Pasport rodinného domu - Donská č.p. 868, Liberec XXX - Vratislavice nad Nisou	
Objekt:	Stavební část	
Výkres:	Půdorys 1.NP - stávající stav	

Ing. Radim Hladký

projektová činnost ve výstavbě

Český Dub, Na Žižkově 154 / IV
+420 734 483 208
radim-hladky@seznam.cz

Formát:

594 x 297

Datum:

04/2026

Stupeň:

Pasport

Měřítko:

1:50

Číslo výkresu:

D.1-02