

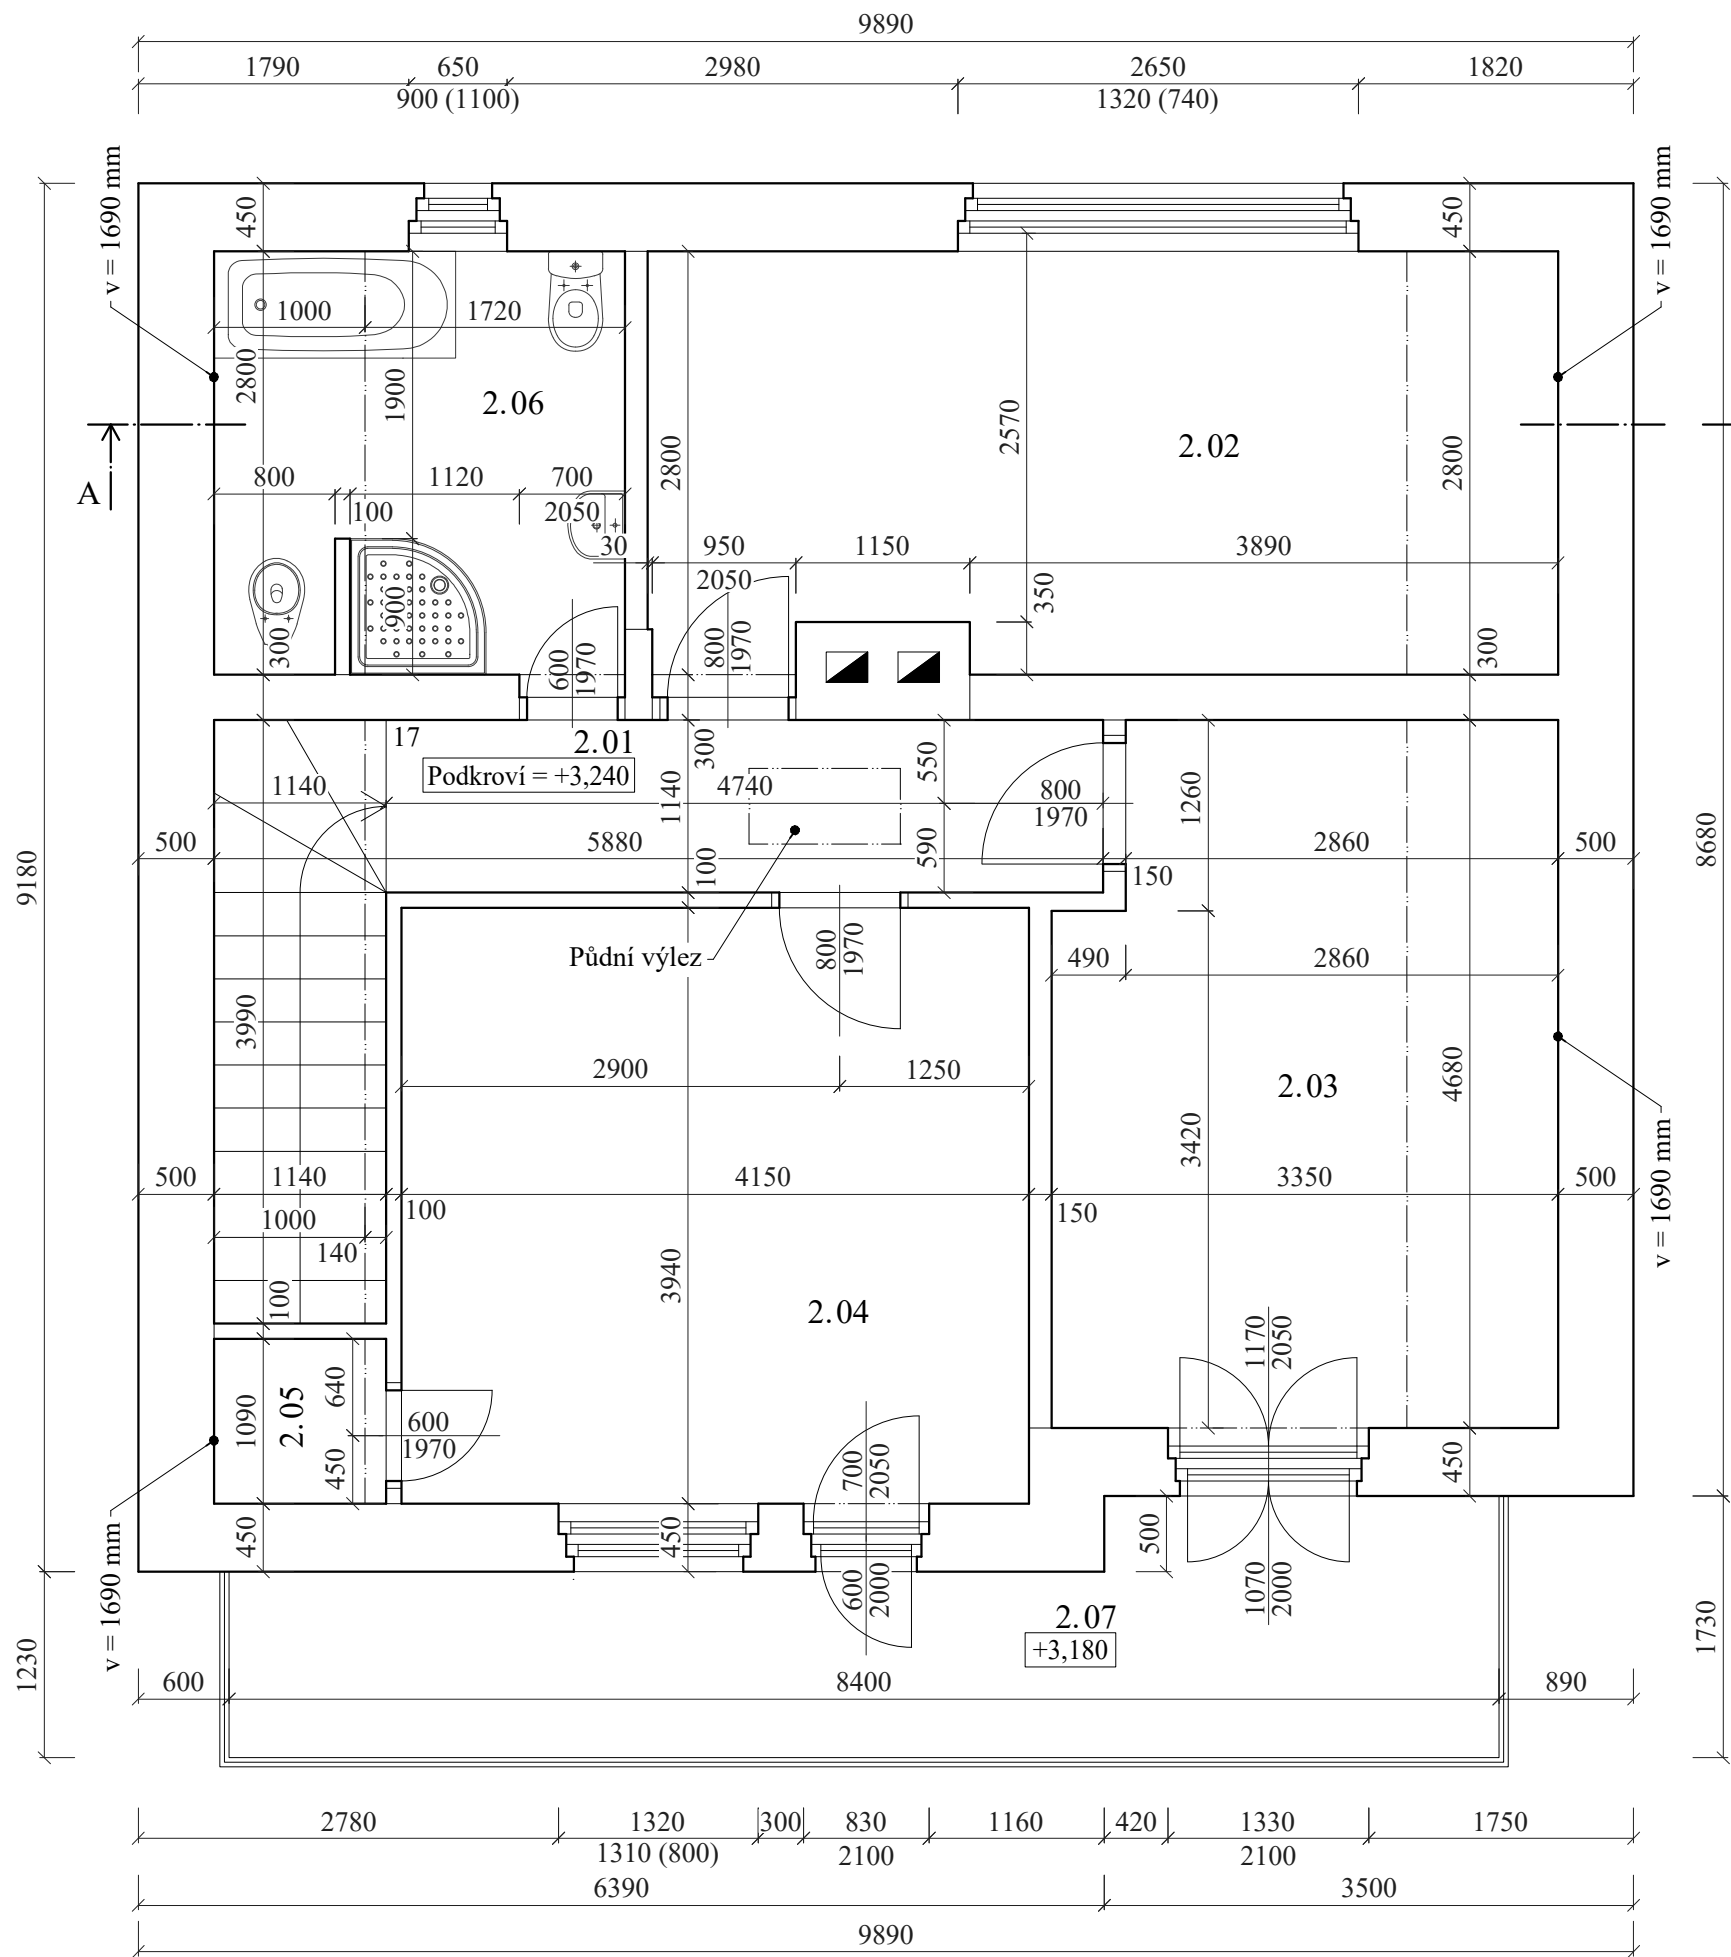


Půdorys podkroví - stávající stav

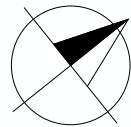

TABULKA MÍSTNOSTÍ					
Číslo místn.	Název místnosti	Plocha [m²]	Výška místnosti	Podlaha	Poznámka
2.01	Kuchyně	5,40	2250 mm	Povlaková krytina	Kera. obklad za původní kuch. linkou
2.02	Pokoje	16,44	2420 mm	Dřevěné vlysy	Šikmina střechy
2.03	Pokoje	15,06	2350 mm	Dřevěné vlysy	Šikmina střechy
2.04	Pokoje	16,35	2350 mm	Dřevěné vlysy	
2.05	Komora	1,24	2350 mm	Dřevěné vlysy	Šikmina střechy
2.06	Koupelna	7,53	2420 mm	Keramická dlažba	Kera. ob., v=2100 mm; šikmin. střechy
2.07	Balkon	11,64	- - -	Keramická dlažba	

LEGENDA KONSTRUKCÍ:

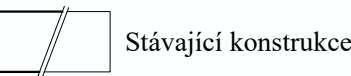

1.NP = ±0.000
= STÁVAJÍCÍ

Vedoucí projektant:		Zodp. projektant:		Vypracoval:		Ing. Radim Hladký projektová činnost ve výstavbě	
Ing. Radomír Hladký		Ing. Radomír Hladký		Ing. Radim Hladký			
Stavebník:		Ing. Lenka Kubínková, Donská 1261, Liberec XXX-Vratislavice nad Nisou, 46311 Liberec				Český Dub, Na Žižkově 154 / IV ☎ +420 734 483 208 ✉ radim-hladky@seznam.cz	
Místo stavby:		p.p.č. 2174, k.ú. Vratislavice nad Nisou [785644]					
Akce:		Pasport rodinného domu - Donská č.p. 868, Liberec XXX - Vratislavice nad Nisou				Formát: 420 x 297	
Objekt:		Stavební část				Datum: 04/2026	
Výkres:		Půdorys podkroví - stávající stav				Stupeň: Pasport	
						Měřítko: 1:50	