



Půdorys střechy - stávající stav

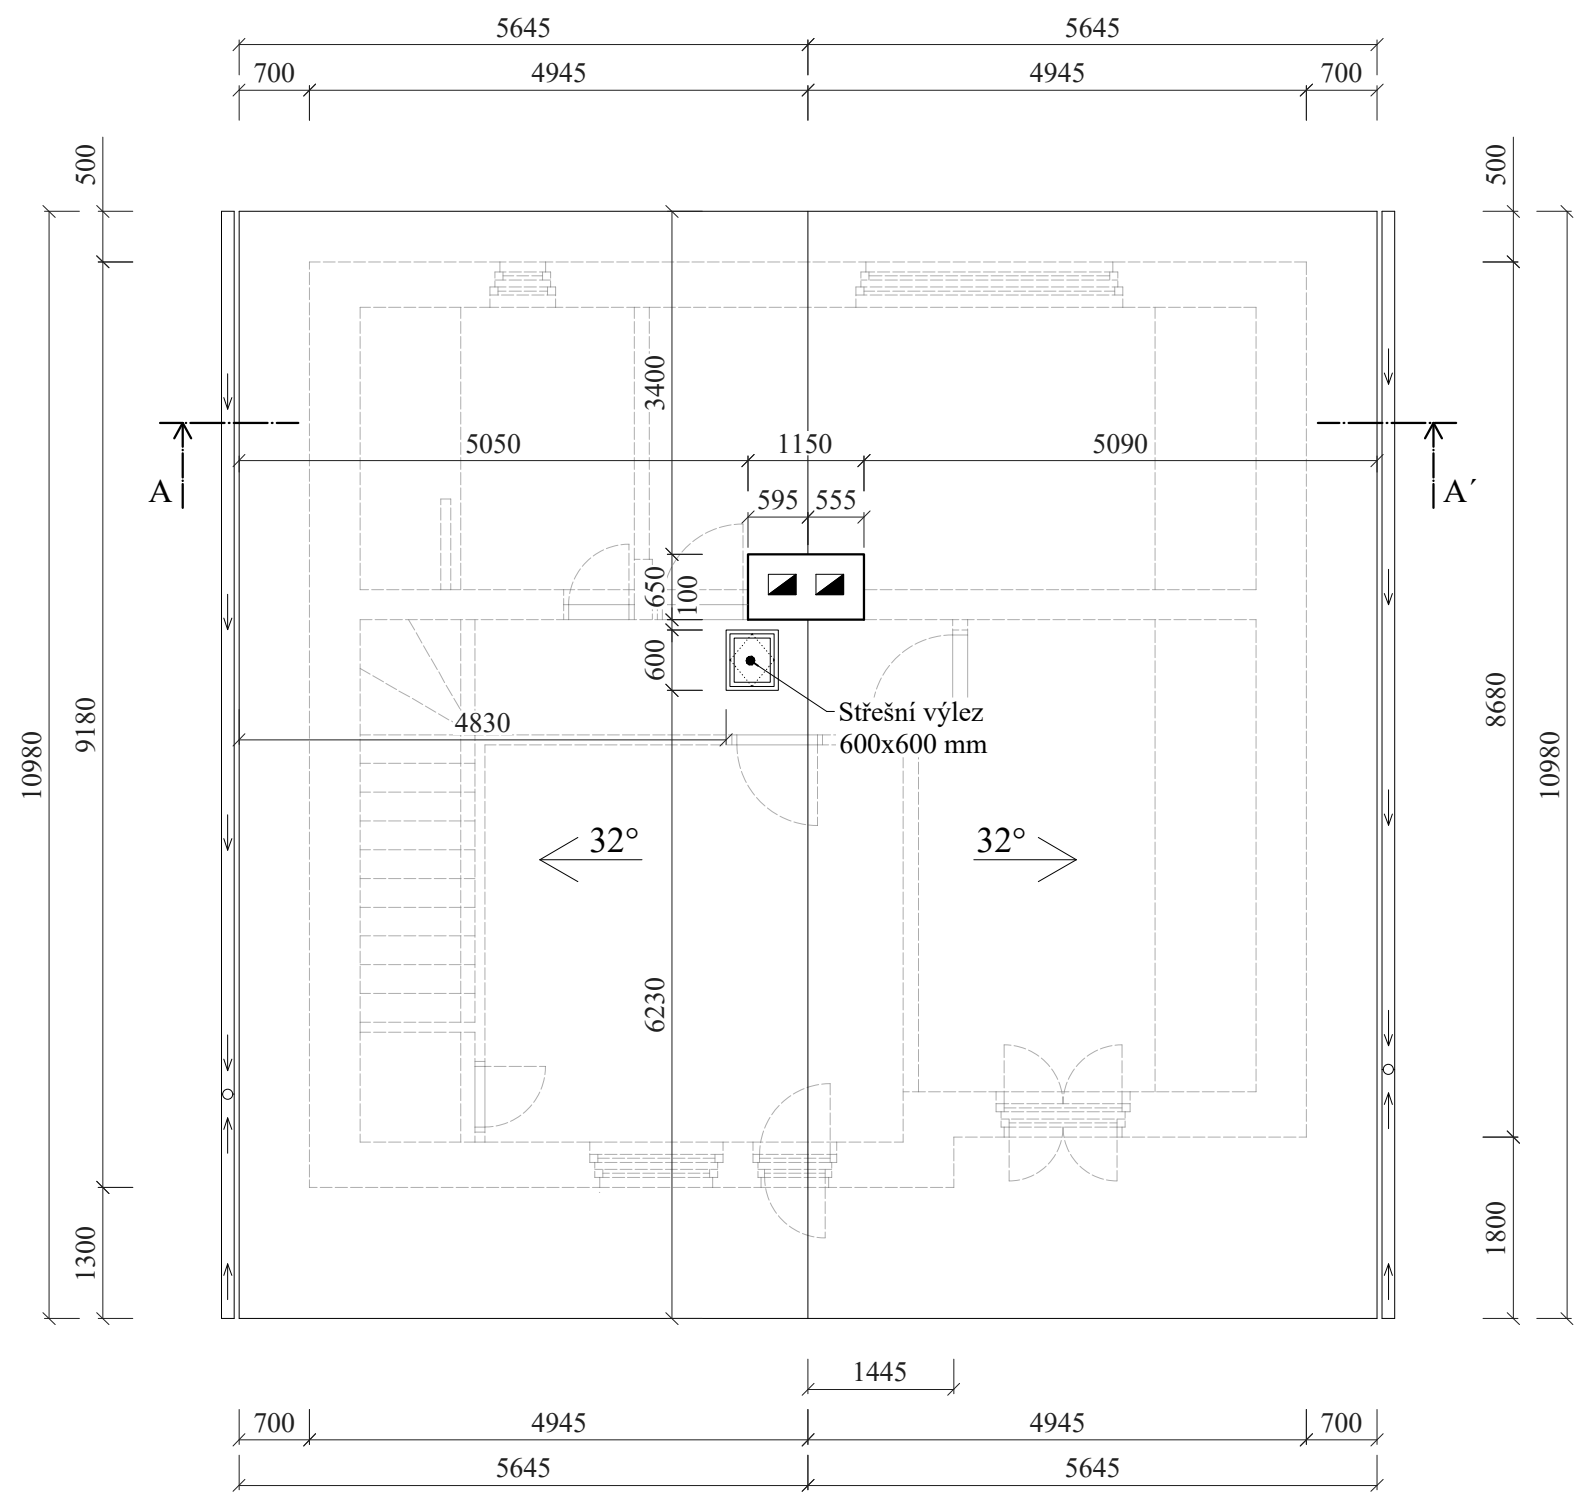

LEGENDA KONSTRUKCÍ:

 Stávající konstrukce

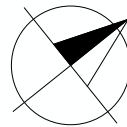

1.NP = ±0.000
= STÁVAJÍCÍ

Vedoucí projektant:		Zodp. projektant:		Vypracoval:		Ing. Radim Hladký projektová činnost ve výstavbě Český Dub, Na Žižkově 154 / IV ☎ +420 734 483 208 ✉ radim-hladky@seznam.cz	
Ing. Radomír Hladký		Ing. Radomír Hladký		Ing. Radim Hladký			
Stavebník:		Ing. Lenka Kubínková, Donská 1261, Liberec XXX-Vratislavice nad Nisou, 46311 Liberec				Formát: 420 x 297	
Místo stavby:		p.p.č. 2174, k.ú. Vratislavice nad Nisou [785644]					
Akce:		Pasport rodinného domu - Donská č.p. 868, Liberec XXX - Vratislavice nad Nisou				Datum: 04/2026	
Objekt:		Stavební část				Stupeň: Pasport	
Výkres:		Půdorys střechy - stávající stav				Měřítko: 1:75	
						Číslo výkresu: D.1-04	