


Pohled jihovýchodní - stávající stav

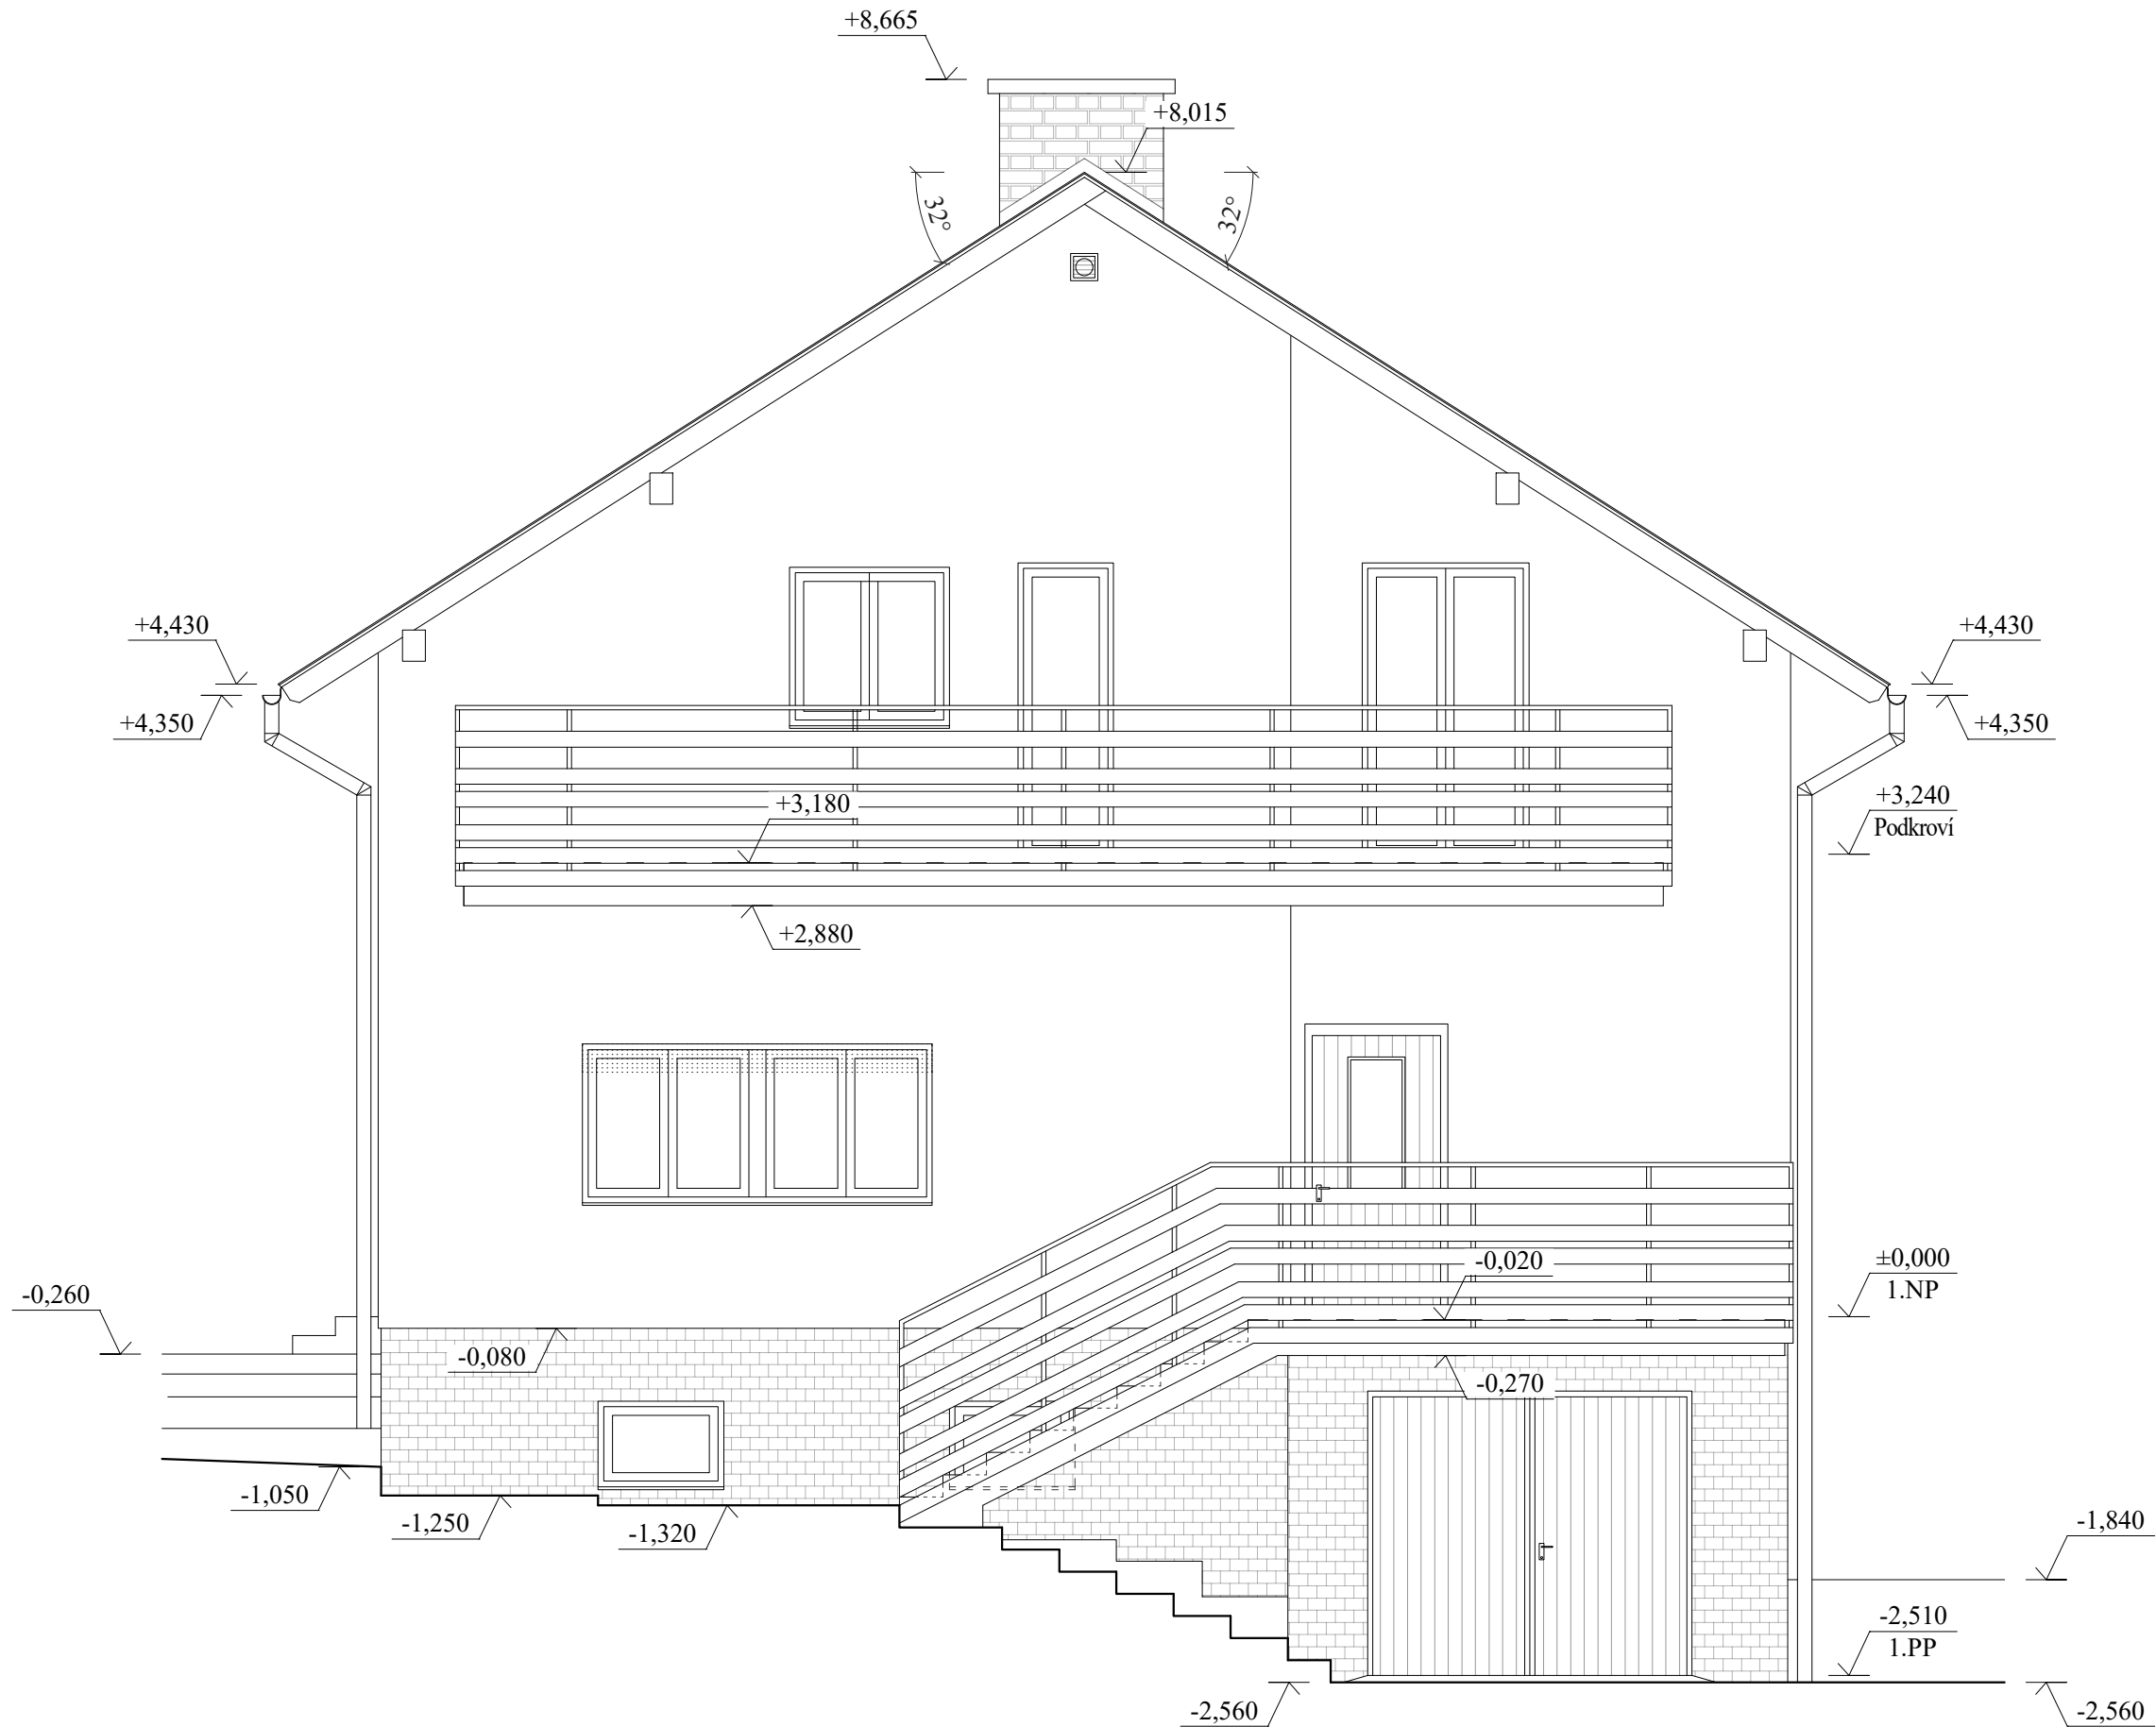

BAREVNÉ ŘEŠENÍ:	
FASÁDA - V PLOŠE	ODSTÍN ŠEDÉ
FASÁDA - SOKL	ODSTÍN ŽLUTÉ - KERA. OBKLAD
VÝPLNĚ OTVORŮ	ODSTÍN HNĚDÉ
TESAŘSKÉ PRVKY	ODSTÍN HNĚDÉ
STŘEŠNÍ KRYTINA	ODSTÍN TMAVĚ ČERVENÉ AŽ HNĚDÉ
KLEMPÍŘSKÉ PRVKY	ODSTÍN TMAVĚ ČERVENÉ AŽ HNĚDÉ

1.NP = ±0.000
= STÁVAJÍCÍ

Vedoucí projektant:	Zodp. projektant:	Vypracoval:	Ing. Radim Hladký projektová činnost ve výstavbě Český Dub, Na Žižkově 154 / IV +420 734 483 208 ✉ radim-hladky@seznam.cz
Ing. Radomír Hladký	Ing. Radomír Hladký	Ing. Radim Hladký	
Stavebník:	Ing. Lenka Kubínková, Donská 1261, Liberec XXX-Vratislavice nad Nisou, 46311 Liberec		
Místo stavby:	p.p.č. 2174, k.ú. Vratislavice nad Nisou [785644]		
Akce:	Pasport rodinného domu - Donská č.p. 868, Liberec XXX - Vratislavice nad Nisou		
Objekt:	Stavební část		
Výkres:	Pohled jihovýchodní - stávající stav		Formát: 594 x 297 Datum: 04/2026 Stupeň: Pasport Měřítko: 1:50 Číslo výkresu: D.1-07